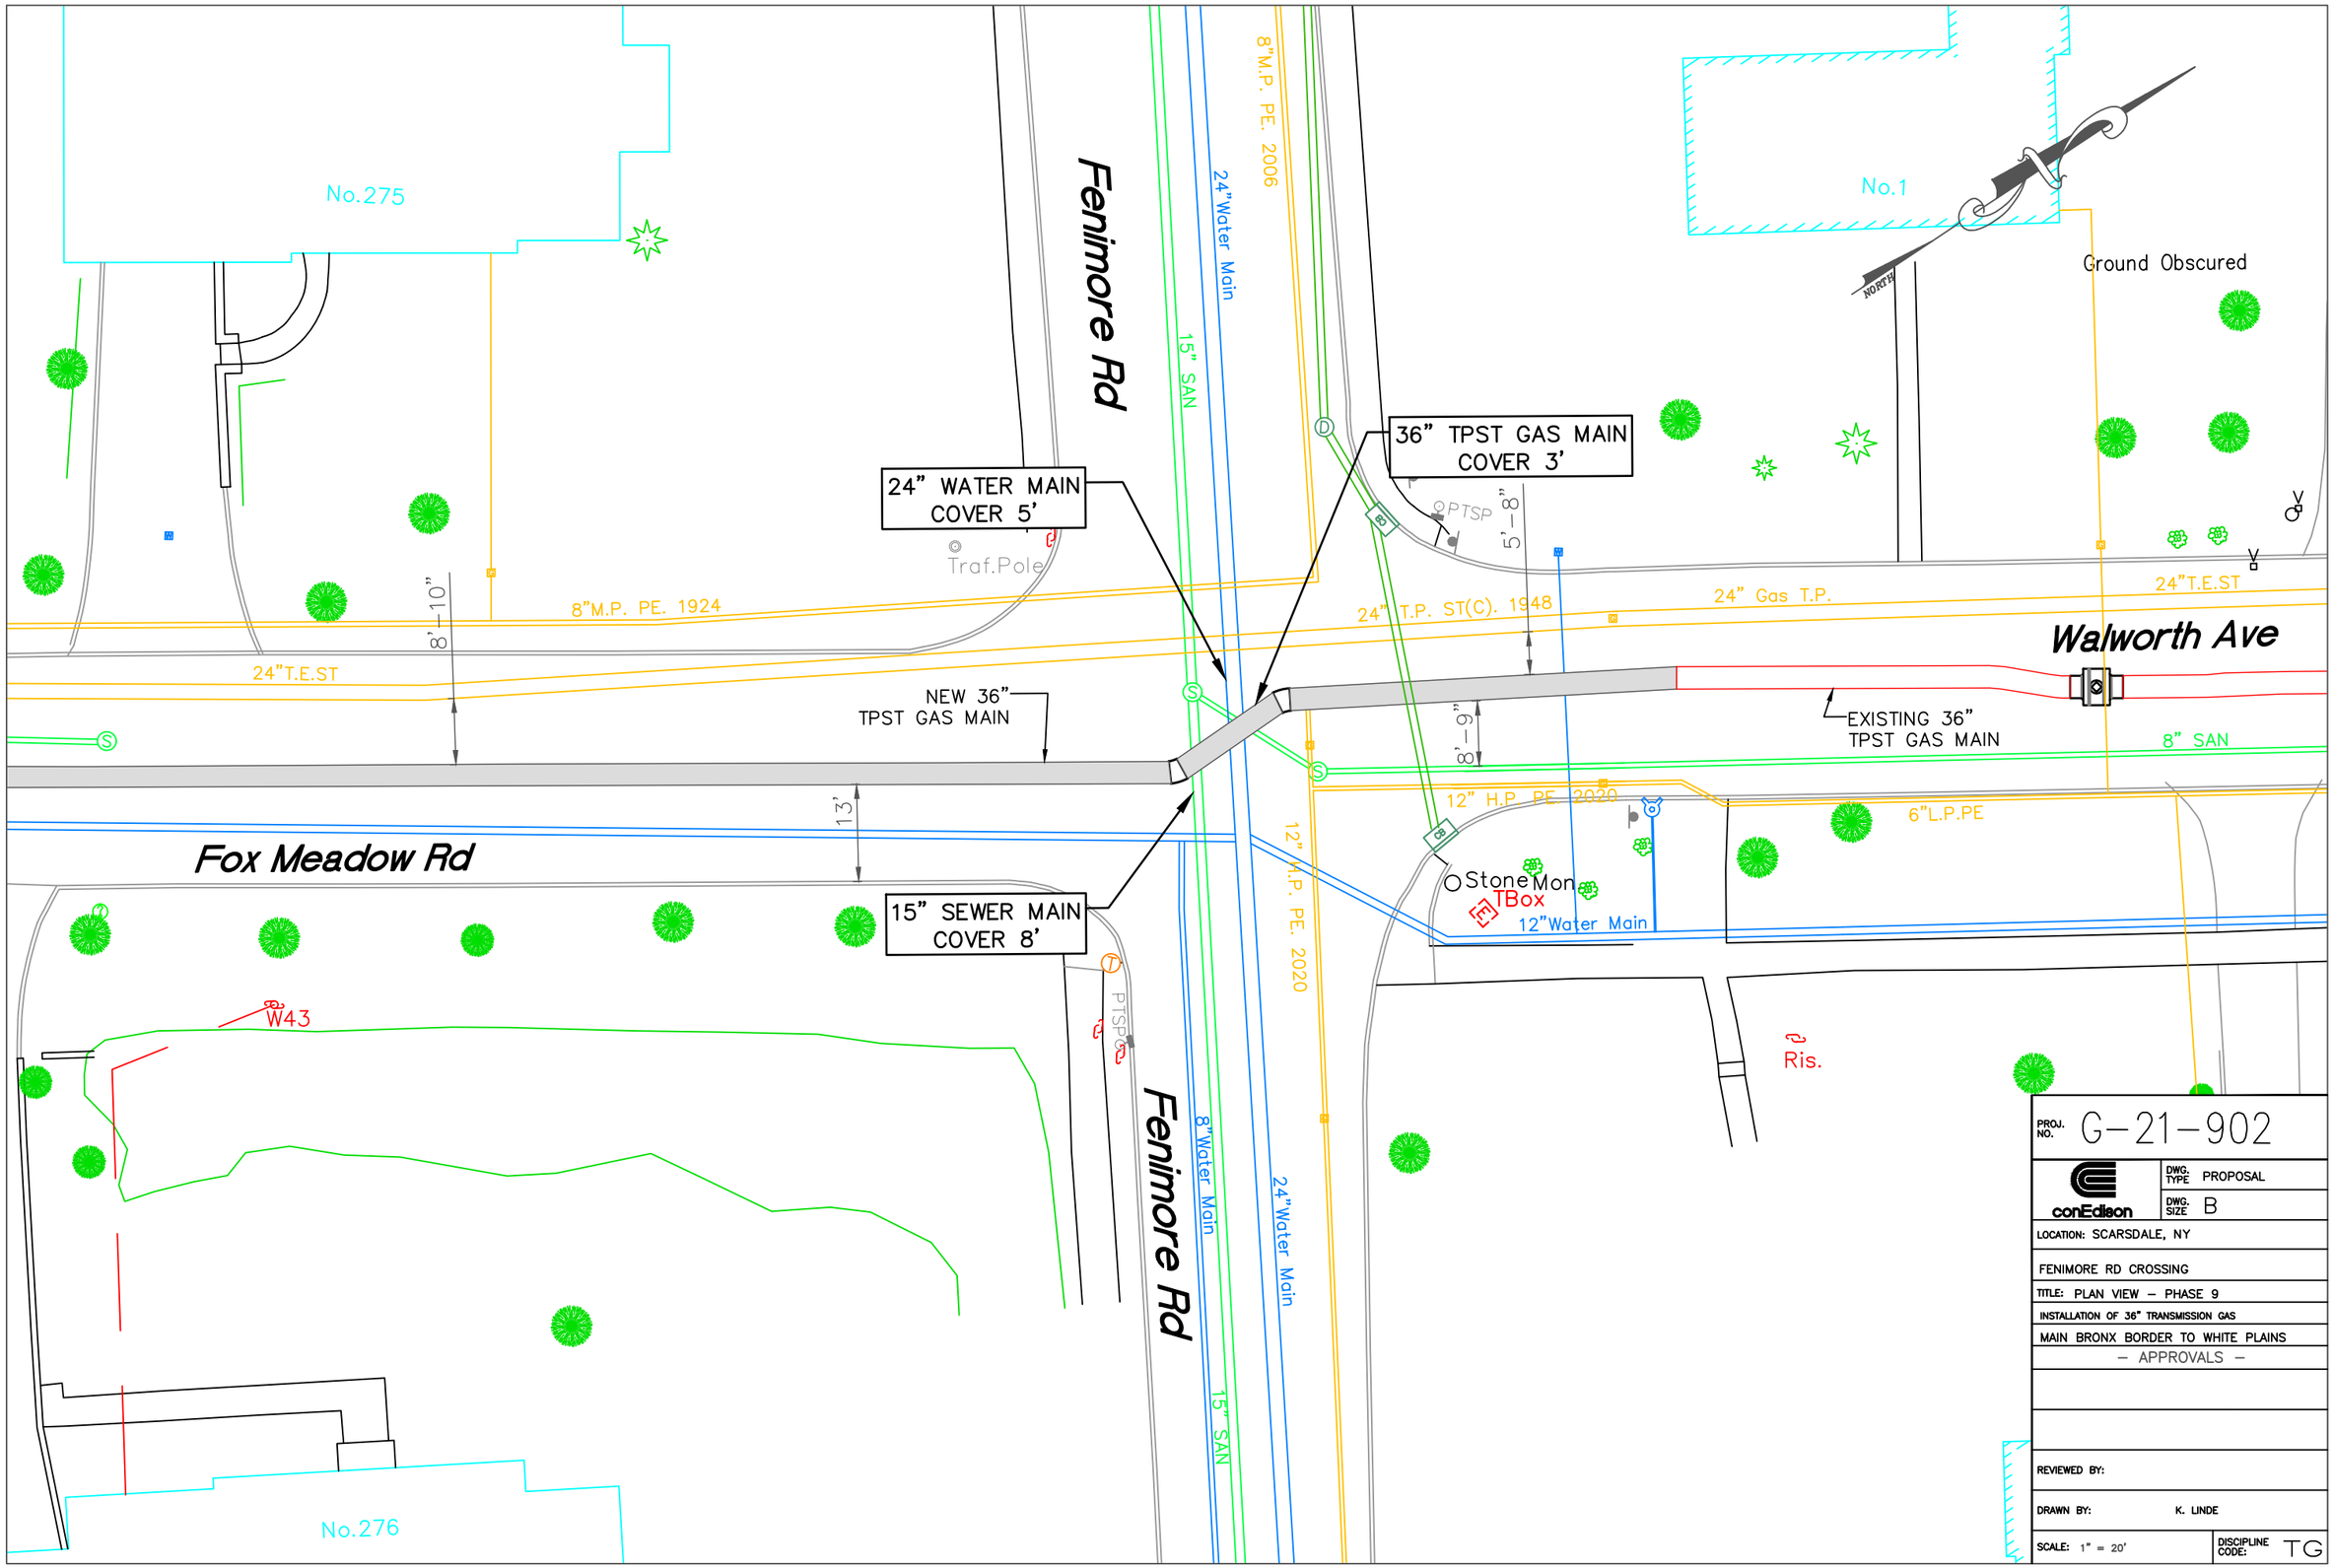

PROJ. NO.	G-21-902
conEdison	DWG. TYPE: PROPOSAL
	DWG. SIZE: B
LOCATION: SCARSDALE, NY	
FENIMORE RD CROSSING	
TITLE: PLAN VIEW – PHASE 9	
INSTALLATION OF 36" TRANSMISSION GAS	
MAIN BRONX BORDER TO WHITE PLAINS	
– APPROVALS –	
REVIEWED BY:	
DRAWN BY:	K. LINDE
SCALE: 1" = 20'	DISCIPLINE CODE: TG